

*АО "ТГК-11"
СП "Энергоремонт"*

*АО "ТГК-11"
СП "ТЭЦ-3"*

Защита ГЩУ ТЭЦ-3 от БПЛА

Рабочая документация

ЗЭ-1246.00

Омск 2025

*АО "ТГК-11"
СП "Энергоремонт"*

*АО "ТГК-11"
СП "ТЭЦ-3"*

Защита ГЩУ ТЭЦ-3 от БПЛА


Рабочая документация

ЗЭ-1246.00

Главный инженер проекта

Л.А. Копченков

Омск 2025

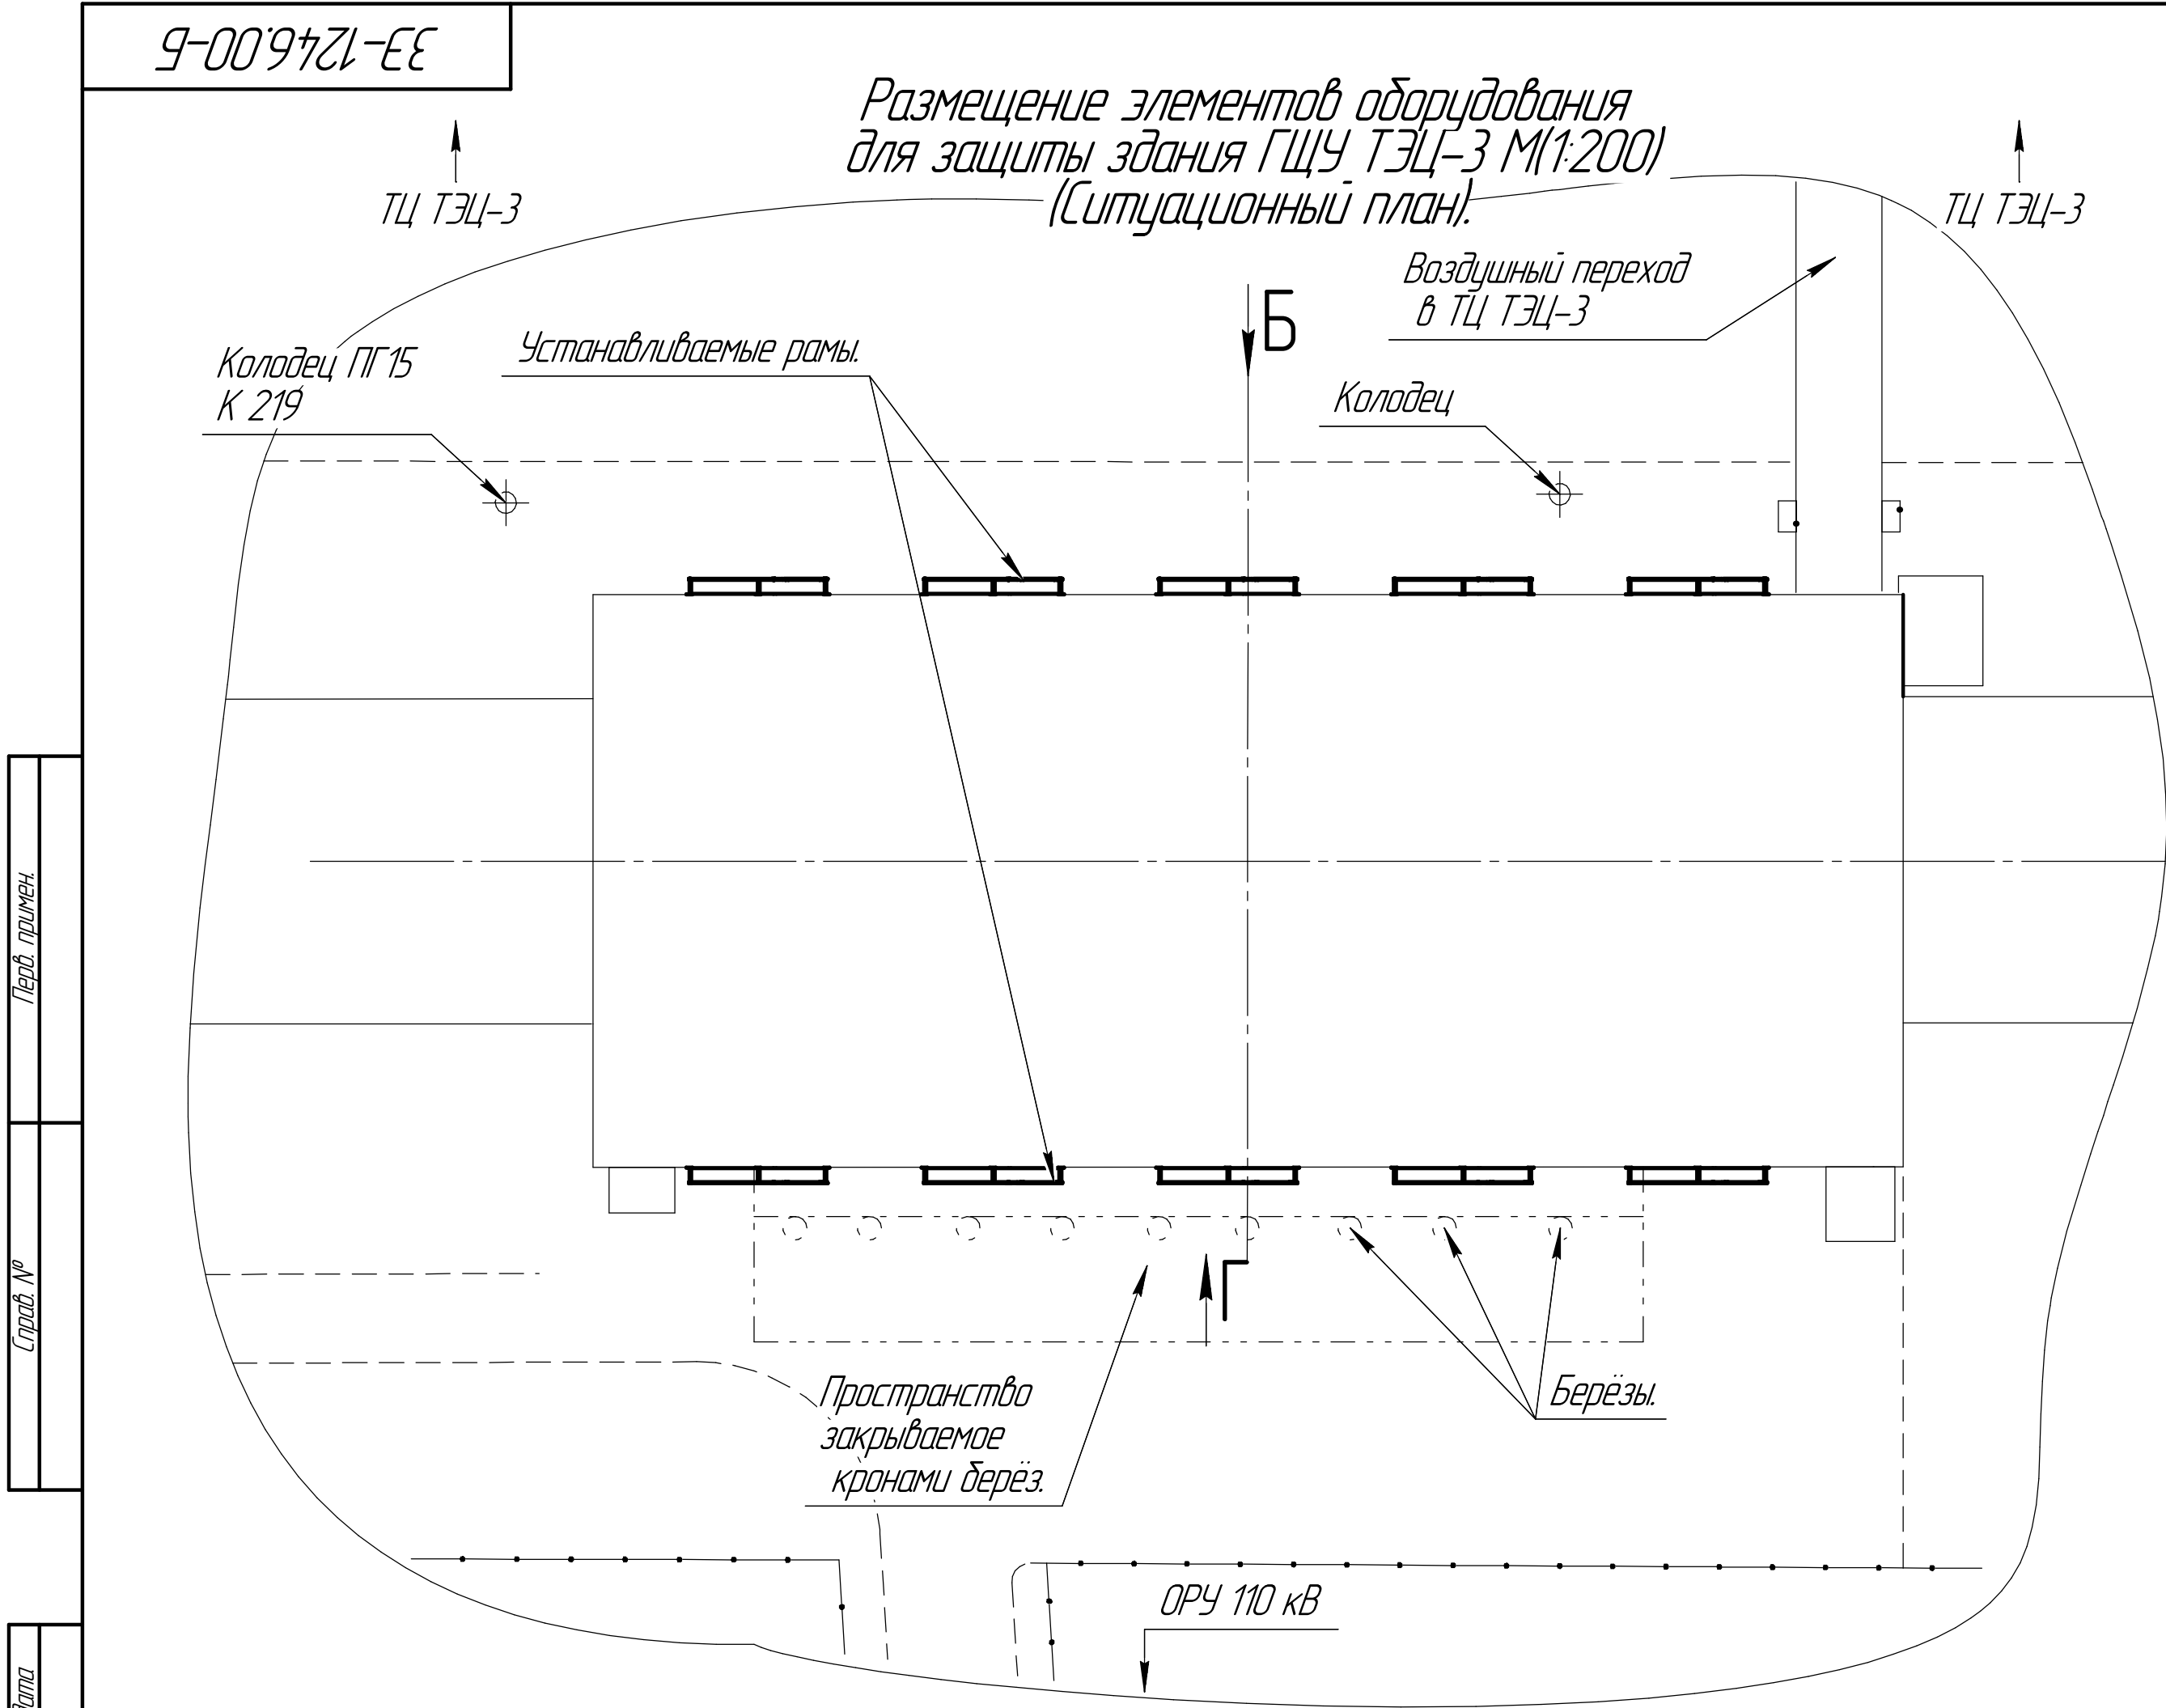

- 1 * Размер для справок.

2 ** Размер уточнить при монтаже.

3 Тонкими линиями указаны элементы здания.

4 Неуказанные предельные отклонения Н16, h16, ± $\frac{IT16}{2}$

5 Заусенцы и острые кромки притупить радиусом 3 мм.

6 Сварные швы выполнить по ГОСТ 5264-80 по линии прилегания элементов. Катет шва должен быть равен меньшей толщине элемента в месте сопряжения. Электрод Э-42 по ГОСТ 9467-75.

7 Обеспечить свободное открытие и закрытие калитки.

8 Разность диагоналей рамы не более 5 мм.

9 Просверленные каналы под установку анкеров заполнить на треть глубины цементно-песчаным раствором.

10 Раму закрывать сеткой как с лицевой стороны так и с торцов.

11 Окрасить металлоконструкции грунтом ГФ-21 в один слой и эмалью ПФ-115 в два слоя.

12 Металлоконструкцию заземлить к существующей системе заземления не менее чем в двух точках с помощью поз. 22.

13 Перед сваркой контура заземления зачистить до металла поз. 22 в месте приварки. После приварки восстановить покрытие "Цинолом".

14 Внутренние стороны стёкол окон оклеить плёнкой поз. 21 в один слой как с фасада так и с тыльной стороны здания.

15 Проект разработан на основе СП 54.2.1325800.2024.

Формат	Зона	Поз	Обозначение	Наименование	Кол	Приме- чание
				Детали		
пч		1	33-1246.01-Б	Стойка L=500 мм	120	шт.
				Уголок 75х6 ГОСТ 8509-93 Ст3сп ГОСТ 535-2005		227 кг
пч		2	33-1246.02-Б	Основание стойки 200х200 мм	120	шт.
				10 ГОСТ 19904-2015 Лист ВСтЗ ГОСТ 14637-2024		377кг
бч		3	33-1246.03-Б	Планка 50х20х3 мм	40	шт.
				Б-ПН-3 ГОСТ 19903-2015 Лист ВСтЗ ГОСТ 16523-97		1 кг
пч		4	33-1246.04-Б	Втулка шарнира	20	шт 3,06кг
пч		5	33-1246.05-Б	Ось шарнира	20	шт 4,66кг
				Стандартные изделия		
		8		Шарик d 11 мм ГОСТ 3722-81	20	шт
				Прочие изделия		
		11		Высоконагруженный анкер 24х180мм М16	480	шт 1382 кг
		12		Крючок ветровой оцинкованный L=75 мм	10	шт 0,3 кг
		14		Винты для крепления крючка поз. 12 к уголку поз. 17	40	шт 0,08 кг
				Материалы		
		17		Уголок 50х5 ГОСТ 8509-93 Ст3сп ГОСТ 535-2005	430	п.м. 1621 кг
		18		Уголок 25х4 ГОСТ 8509-93 Ст3сп ГОСТ 535-2005	200	п.м. 224 кг
		19		Сетка 2-50-3,0-0 ГОСТ 5336-80	360	м ² 872 кг
		20		Проволока 4-1570-В ГОСТ 7372-79	650	п.м. 65 кг
		21		Бронеплёнка противоосколочная толщина 200 мкм	162	м ²
		22		Полоса оцинков. 5х50 ГОСТ 103-2006 Ст3сп ГОСТ 535-2005	80	п.м. 157 кг
				33-1246.00-Б		
				Защита ГЩУ ТЭЦ-3 от БП/А.	Лит	Масса
						4 941кг.
					Лист 1	Листов 5
					КТО СИС ИЦ СП "Энергоремонт" АО "ТГК-11"	
Изм.	Лист	№ докум.	Подп.	Дата		
Разраб.	Белодорогов					
Пров.	Балов					
Г.контр.						
Н.контр.	Балов					
Утв.	Иванов					
Копировал					Формат А2	

Б(1:100) ○(1) Вид со стороны ТЦ.



Изд. № подл.	Подп. и дата
Взам. инв. №	Изд. № эф. №
Подп. и дата	Подп. и дата

Изм.	Лист	№ докум.	Подп.	Дата
------	------	----------	-------	------

33-1246.00-Б

Копировал


Формат А2

Лист
2

Г(1:100)(1) Вид со стороны ОРУ 110кВ



Изд. №	Подп. и дата	Взам. инд. №	Изд. №	Подп. и дата
подл.			додл.	

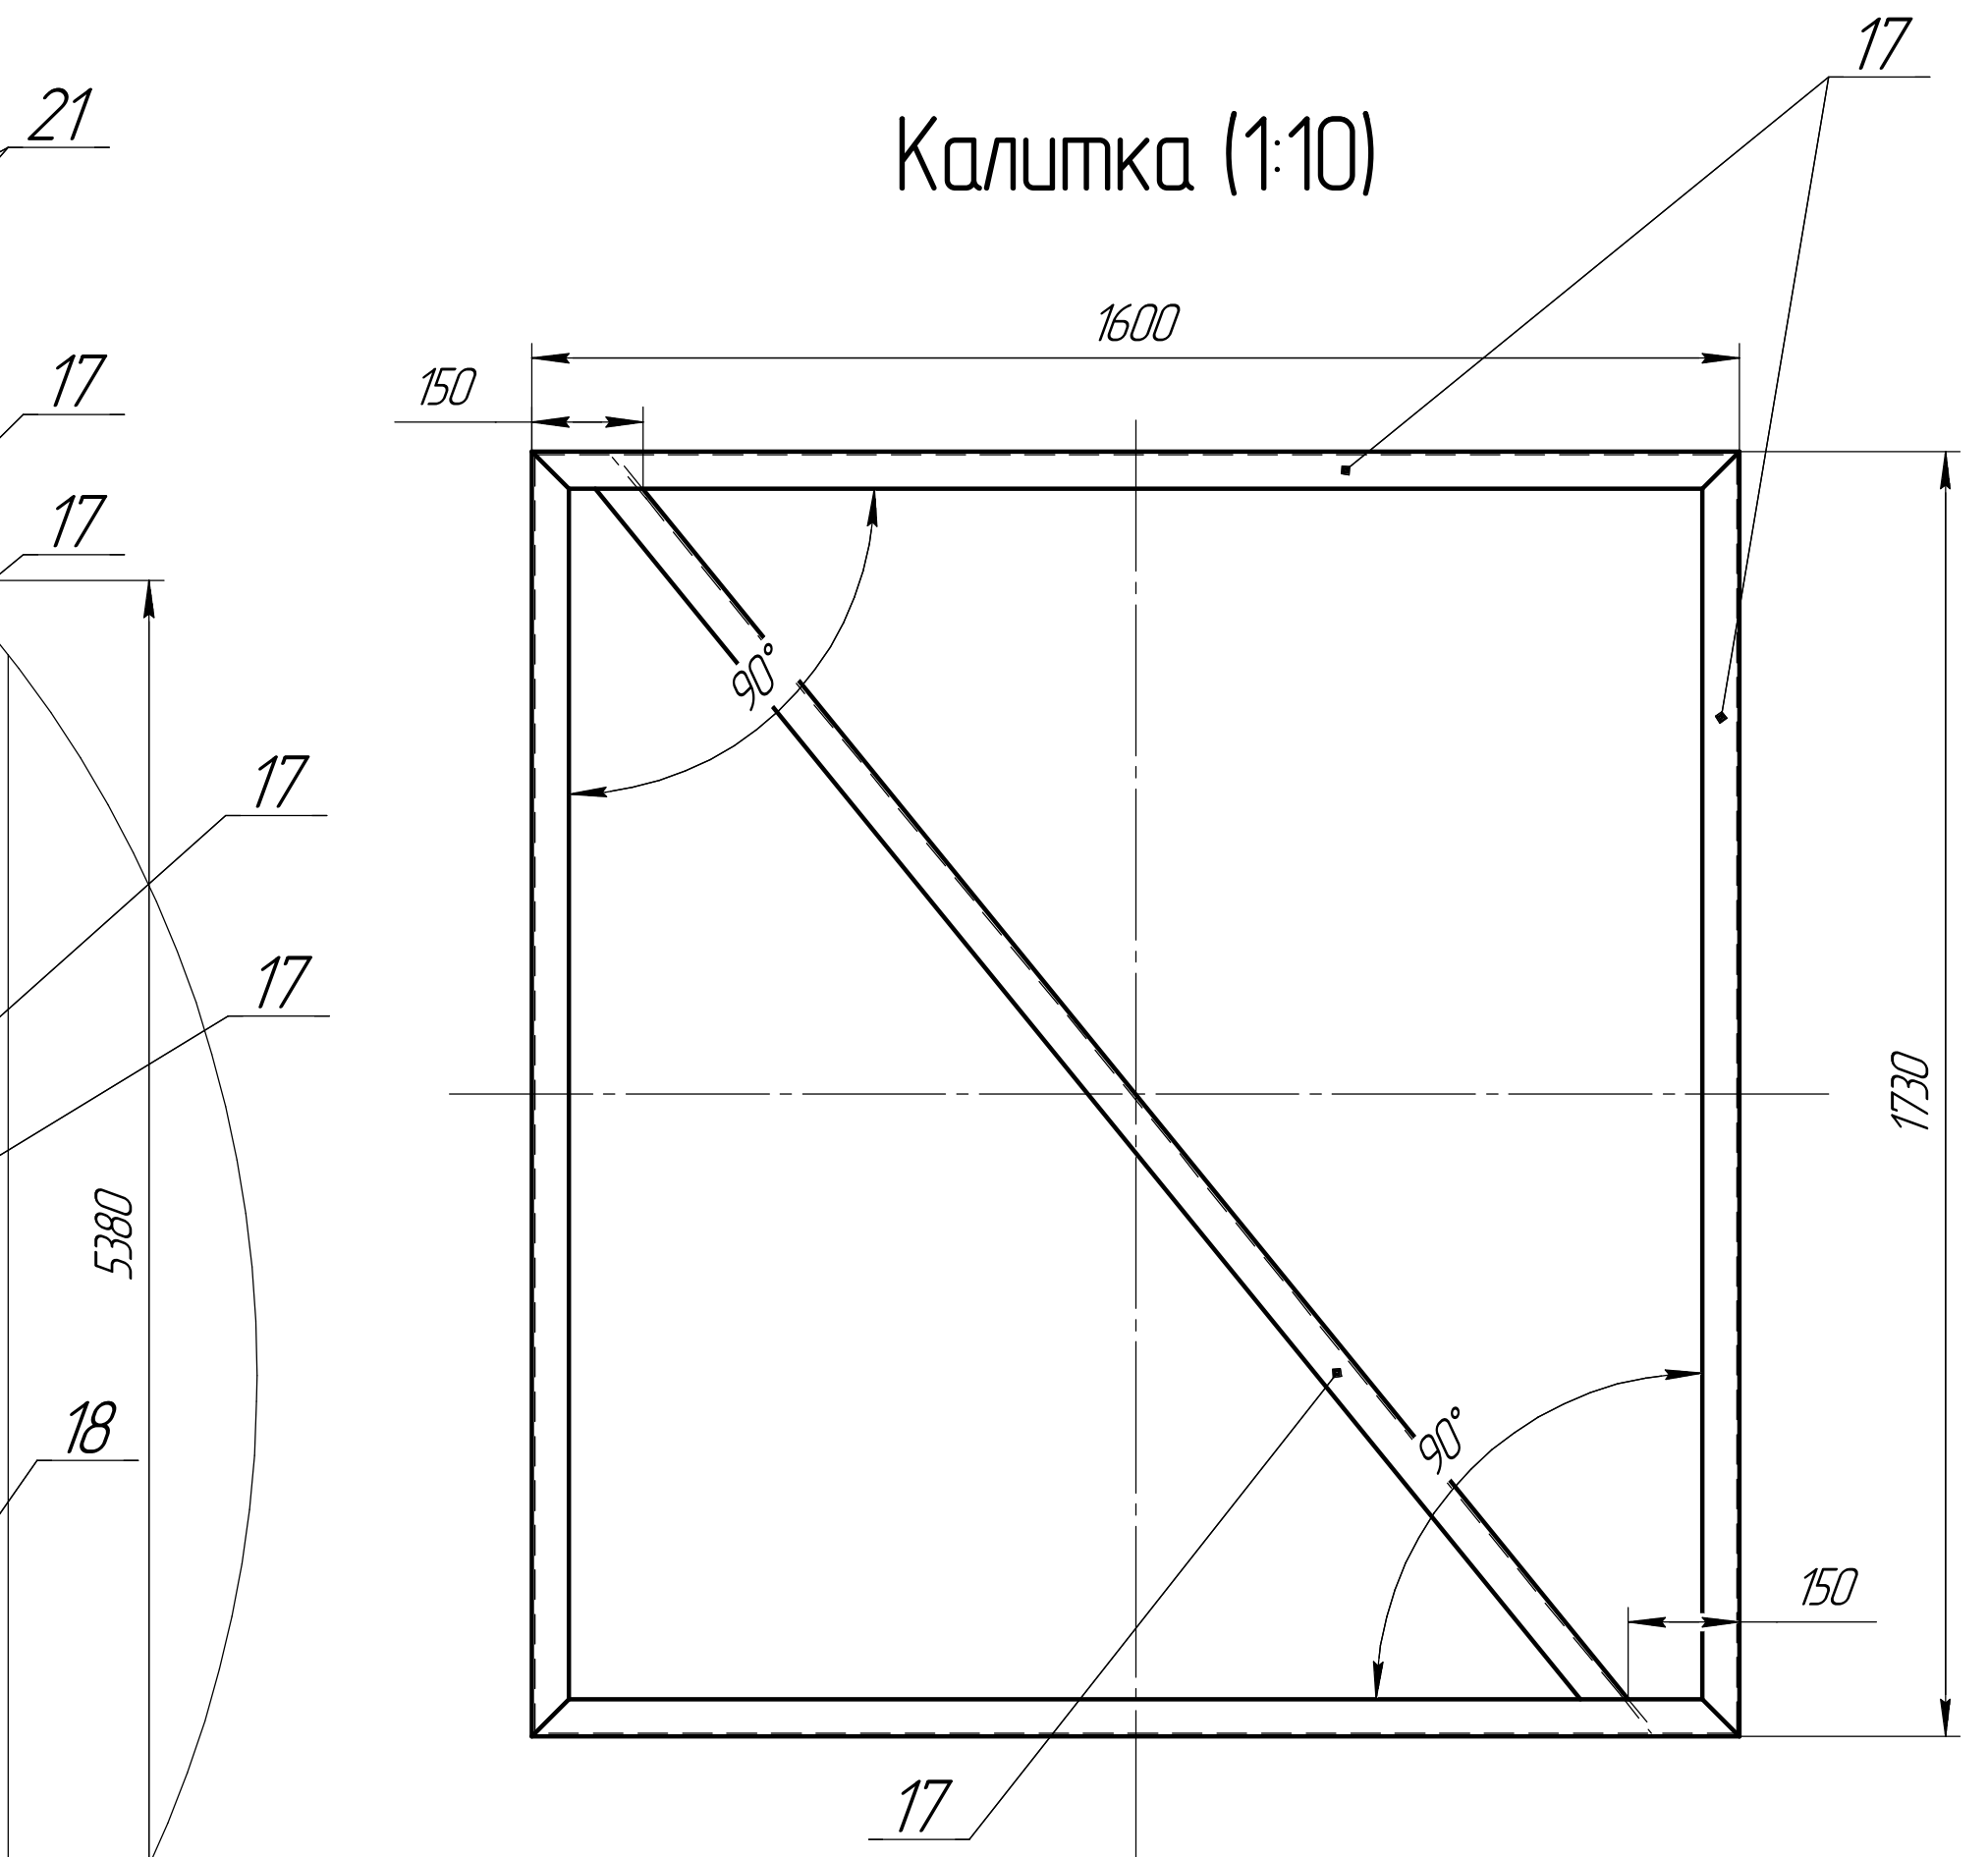

Дет. поз.5 (1:1)
33-1246.05-Б
25 ГОСТ 2590-2006
Круж ВСт3пс2 ГОСТ 535-2005

